


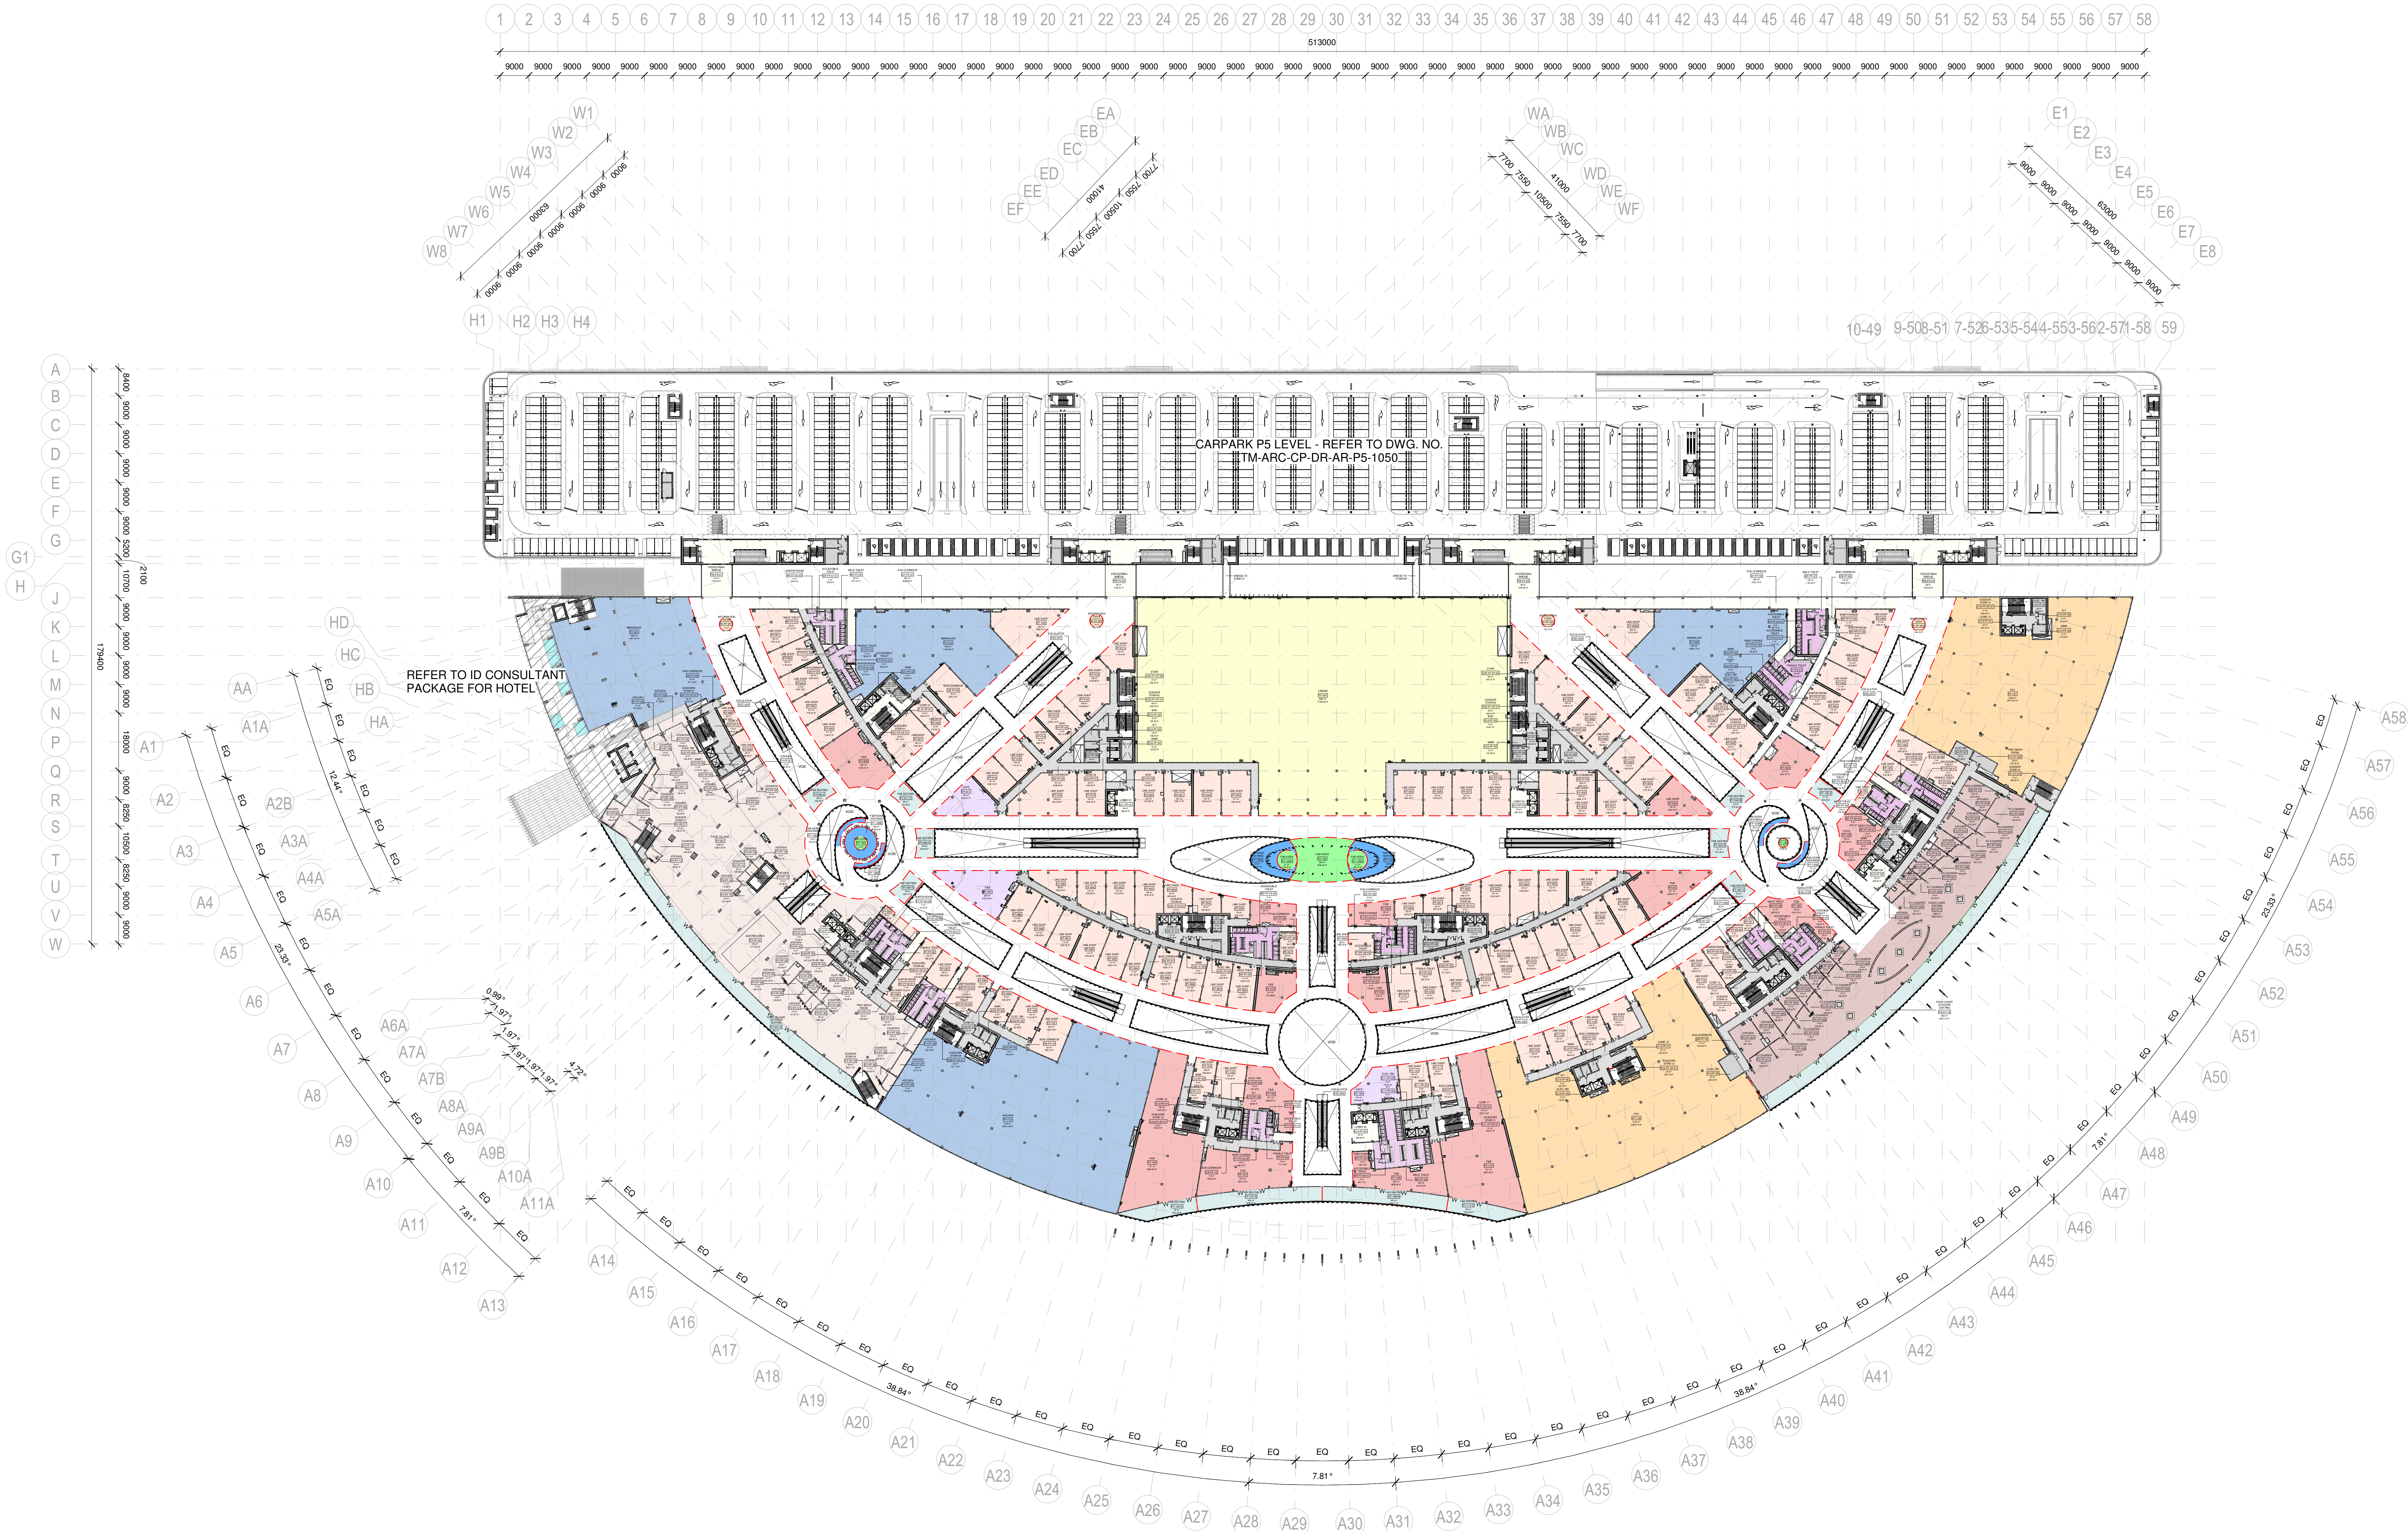

1 FIRST FLOOR - OVERALL LEASING PLAN
7030 1 : 750



GENERAL NOTES:
THIS DRAWING IS TO BE READ IN CONJUNCTION WITH RELEVANT ARCHITECTURAL, STRUCTURAL, MEP AND CIVIL DRAWINGS.
ALL WORKS ARE TO BE CARRIED OUT IN ACCORDANCE WITH ALL RELEVANT BUILDING STANDARDS AND CODES OF PRACTICE AND ALSO MEET THE LOCAL AUTHORITY REQUIREMENTS.
DIMENSIONS ARE NOT TO BE SCALED FROM THIS DRAWING. CONTRACTOR AND THEIR SUBCONTRACTORS ARE TO VERIFY ALL DIMENSIONS ON SITE BEFORE MAKING ANY SHOP DRAWINGS AND BEFORE EXECUTING THE WORKS.
ANY DISCREPANCIES, EITHER BETWEEN WRITTEN DIMENSIONS AND SITE DIMENSIONS OR BETWEEN THIS DRAWING AND OTHER CONSULTANTS OR SUPPLIERS DRAWINGS, SHOULD BE BROUGHT TO THE IMMEDIATE ATTENTION OF THE ARCHITECT BEFORE EXECUTING THE WORKS.

BUILDING AREA LEGEND

- CUSTOMER SERVICE
- CINEMA
- F&B
- F.C. SEATING
- F&B / CAFE
- F&B KIOSK
- F&B KIOSK SEATING AREA
- FC KITCHEN
- RETAIL
- SPECIALTY RETAIL
- FOOD COURT STALL
- FOOD VILLAGE
- FOOD VILLAGE STALL
- FV KITCHEN
- FOOD COURT
- OFFICE AREA
- CIRCULATION
- MEP
- BOH
- TOILET

T1	02/05/19	TENDER ISSUE
P01	28/09/18	FIRST ISSUE
Rev	Date	Description

Purpose of Issue: FOR TENDER

Original Site	A0	Designed By:	CC
Datum	-	Checked By:	EM
Grd	-	Approved By:	RD / CW

Client :
Tilal Mall L.L.C
P.O. Box 5995
Sharjah, UAE
Tel: +971 (6) 5560005
Fax: +971 (6) 5560033

Lead Consultant :
ARCADIS Design & Consultancy
for natural and built assets
Copyright © Arcadis 2018 P.O. Box 52750 Dubai, UAE Tel: +971 (4) 3193333 Fax: +971 (4) 3242331

Sub-Consultant :

Architect / Engineer of record :
ARCADIS Design & Consultancy
for natural and built assets
Copyright © Arcadis 2018 P.O. Box 1779 Sharjah, UAE

Project Name:
Tilal Mall and Hotel
Sharjah, UAE

Plot Number / Area 7040 / JWAIZEI

Drawing Title
MALL FIRST FLOOR, HOTEL FIRST FLOOR,
CARPARK LEVEL P5 OVERALL LEASING
PLAN

Scales	Drawn By	Suitability Code	Project Stage
1:750	CC	S4	TENDER

Drawing No.	Rev.
TM-ARC-ML-DR-AR-1F-7030	T1