


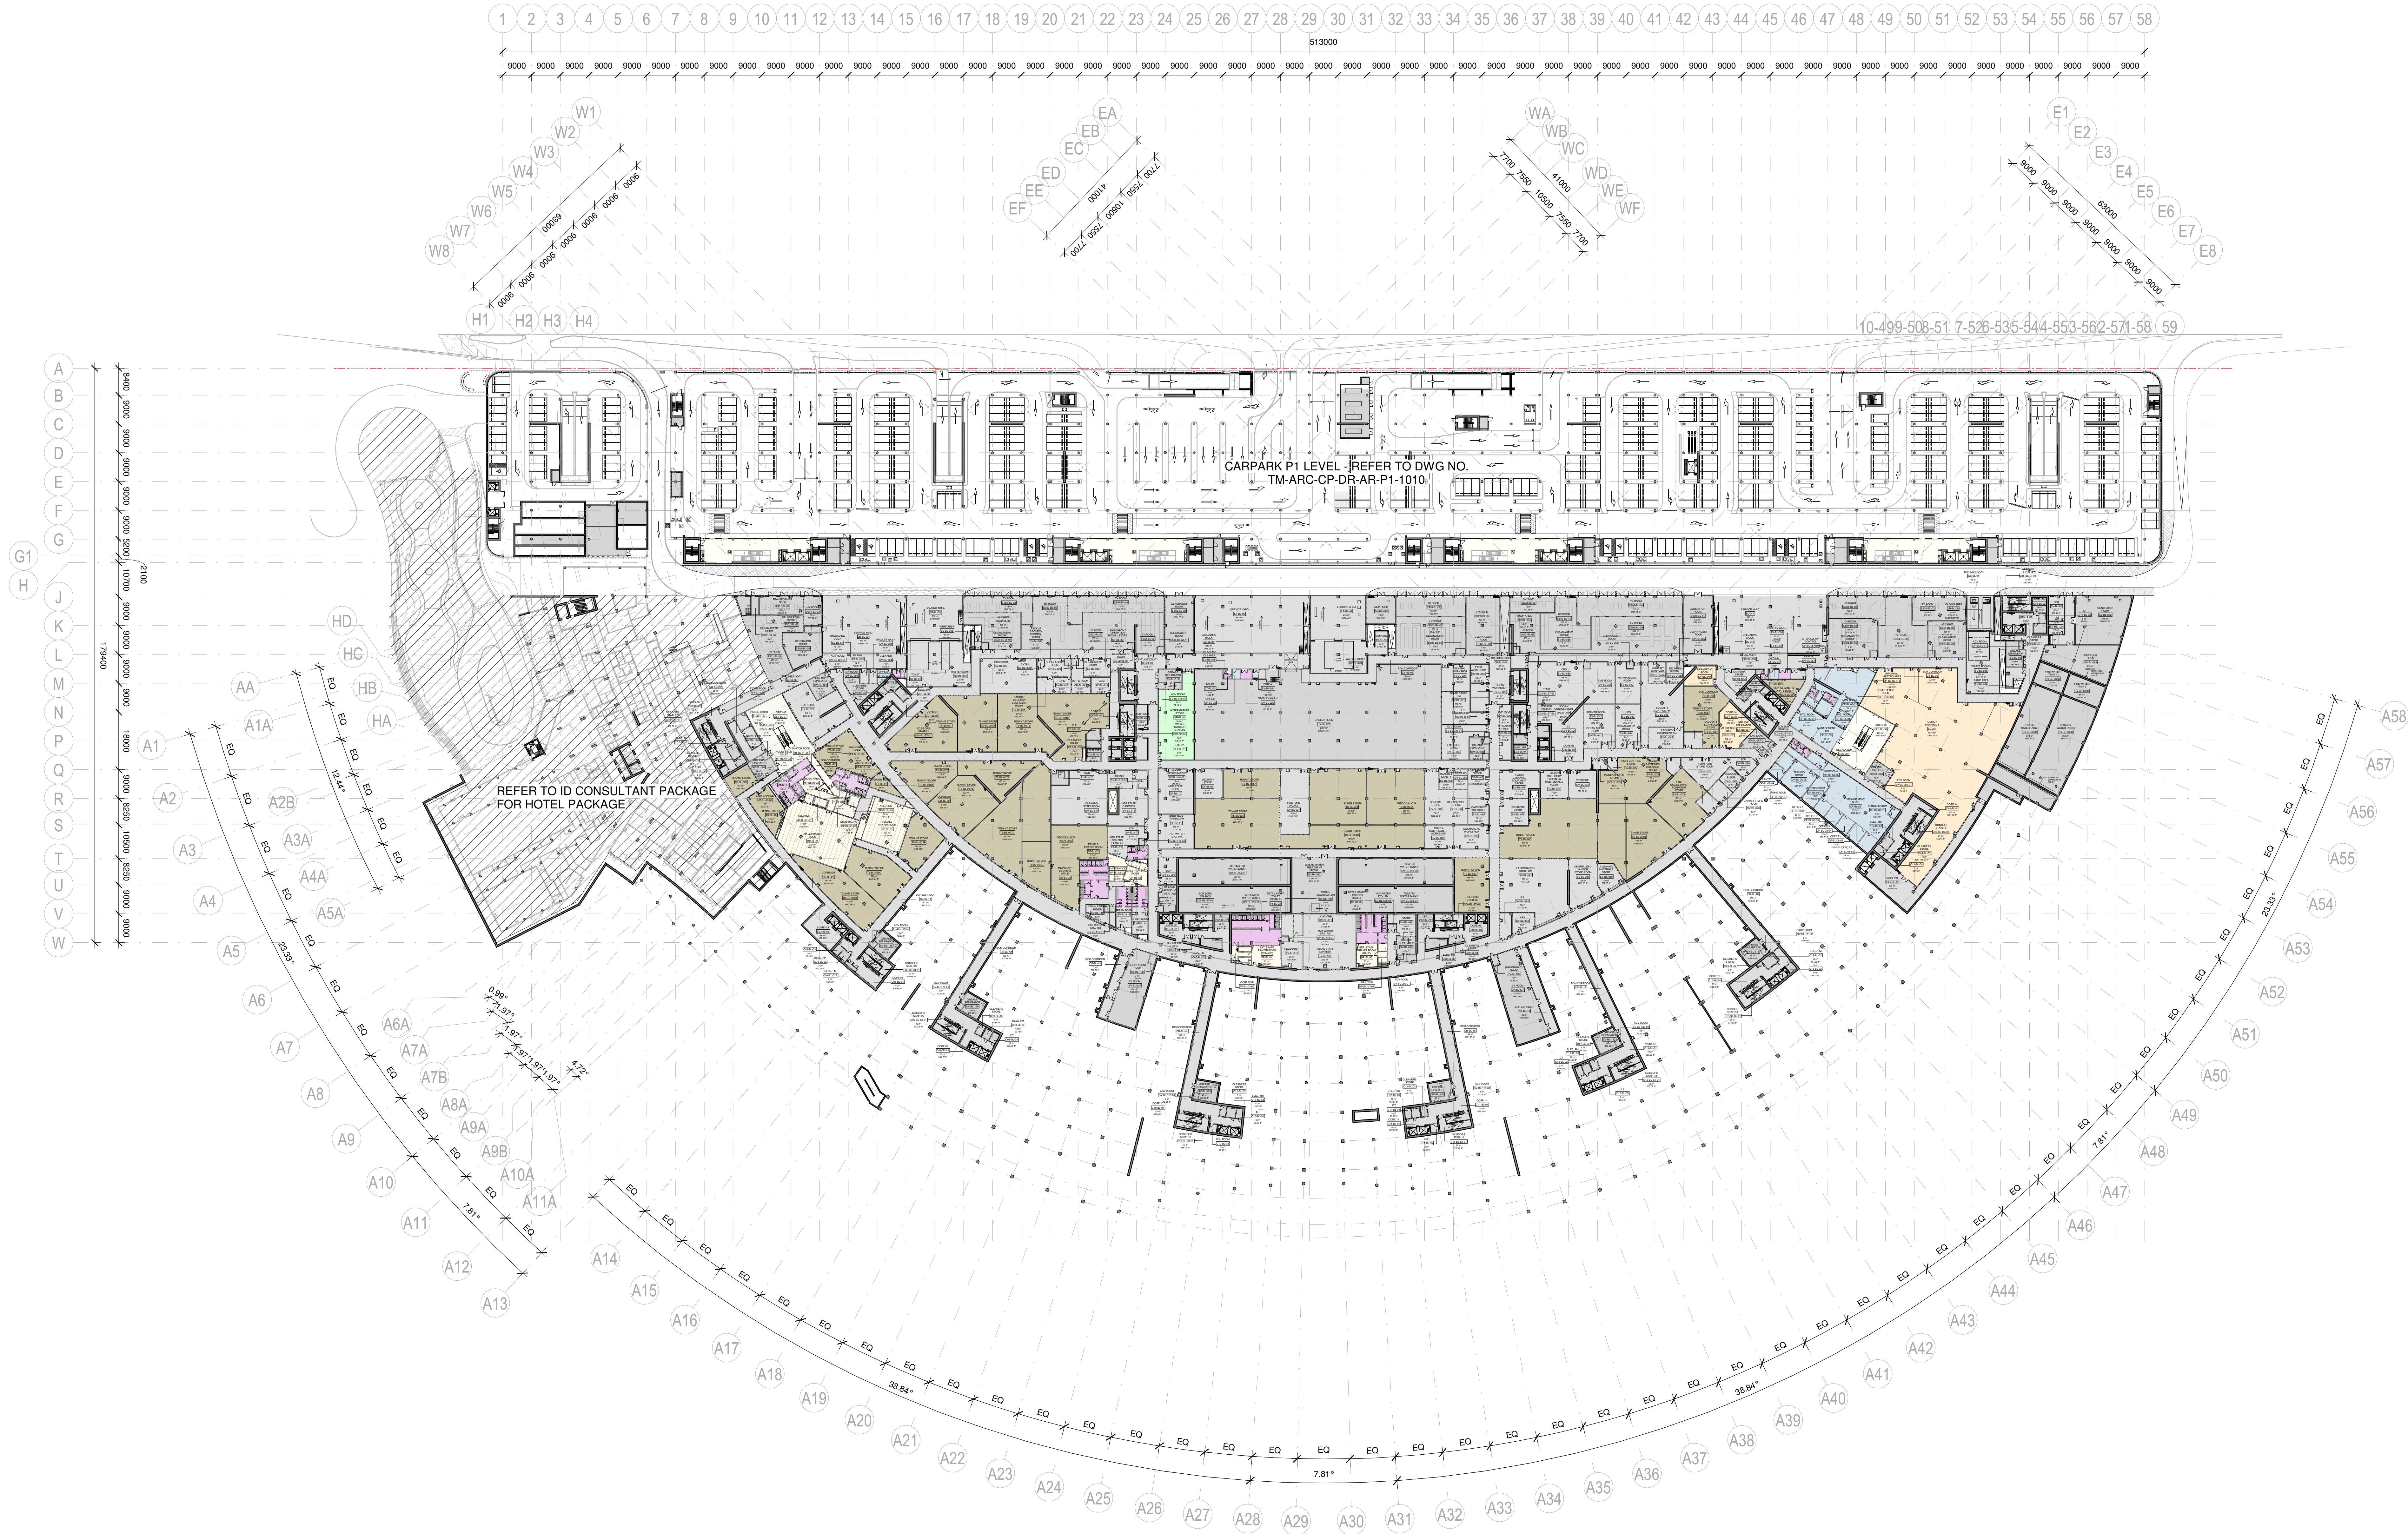

1 BASEMENT - OVERALL LEASING PLAN
7010 1 : 750



GENERAL NOTES:
THIS DRAWING IS PROTECTED BY COPYRIGHT.
THIS DRAWING IS TO BE READ IN CONJUNCTION WITH RELEVANT ARCHITECTURAL, STRUCTURAL, MEP AND CIVIL DRAWINGS.
ALL WORKS ARE TO BE CARRIED OUT IN ACCORDANCE WITH ALL RELEVANT BUILDING STANDARDS AND CODES OF PRACTICE AND ALSO MEET THE LOCAL AUTHORITY REQUIREMENTS.
DIMENSIONS ARE NOT TO BE SCALED FROM THIS DRAWING. CONTRACTOR AND THEIR SUBCONTRACTORS ARE TO VERIFY ALL DIMENSIONS ON SITE BEFORE MAKING ANY SHOP DRAWINGS AND BEFORE EXECUTING THE WORKS.
ANY DISCREPANCIES, EITHER BETWEEN WRITTEN DIMENSIONS AND SITE DIMENSIONS OR BETWEEN THIS DRAWING AND OTHER CONSULTANTS' OR SUPPLIERS' DRAWINGS, SHOULD BE BROUGHT TO THE IMMEDIATE ATTENTION OF THE ARCHITECT BEFORE EXECUTING THE WORKS.

- BUILDING AREA LEGEND**
- CUSTOMER SERVICE
 - MANAGEMENT SUITE
 - PRAYER ROOM
 - HYPERMARKET
 - TENANT STORE
 - CIRCULATION
 - MEP
 - BOH
 - TOILET

T1	02/05/19	TENDER ISSUE
P04	30/01/18	SCHEMATIC ADDENDUM
P03	18/01/18	SCHEMATIC ADDENDUM
P02	17/12/17	100% SCHEMATIC DESIGN ISSUE
P01	16/11/17	50% SCHEMATIC DESIGN
Rev	Date	Description

Purpose of Issue: **FOR TENDER**

Original Site	A0	Designed By:	CCHK
Datum	-	Checked By:	EM
Grid	-	Approved By:	RD / CW

Client :
Tilal Mall L.L.C
P.O. Box 5995
Sharjah, UAE
Tel: +971 (6) 5560055
Fax: +971 (6) 5560033

Lead Consultant:
ARCADIS Design & Consultancy
for natural and built assets
Copyright © Arcadis 2018 P.O. Box 52750 Tel: +971 (4) 3193333
Dubai, UAE Fax: +971 (4) 3242331

Sub-Consultant :

Architect / Engineer of record :
ARCADIS Design & Consultancy
for natural and built assets
Copyright © Arcadis 2018 P.O. Box 1779
Sharjah, UAE

Project Name:
Tilal Mall and Hotel
Sharjah, UAE

Plot Number / Area 7040 / JWAIZEI

Drawing Title
MALL BASEMENT, HOTEL BASEMENT,
CARPARK LEVEL P1 OVERALL LEASING
PLAN

Scales 1:750 Drawn By CCHK Suitability Code S4 Project Stage TENDER

Drawing No. TM-ARC-ZZ-DR-AR-BL-7010 Rev. T1